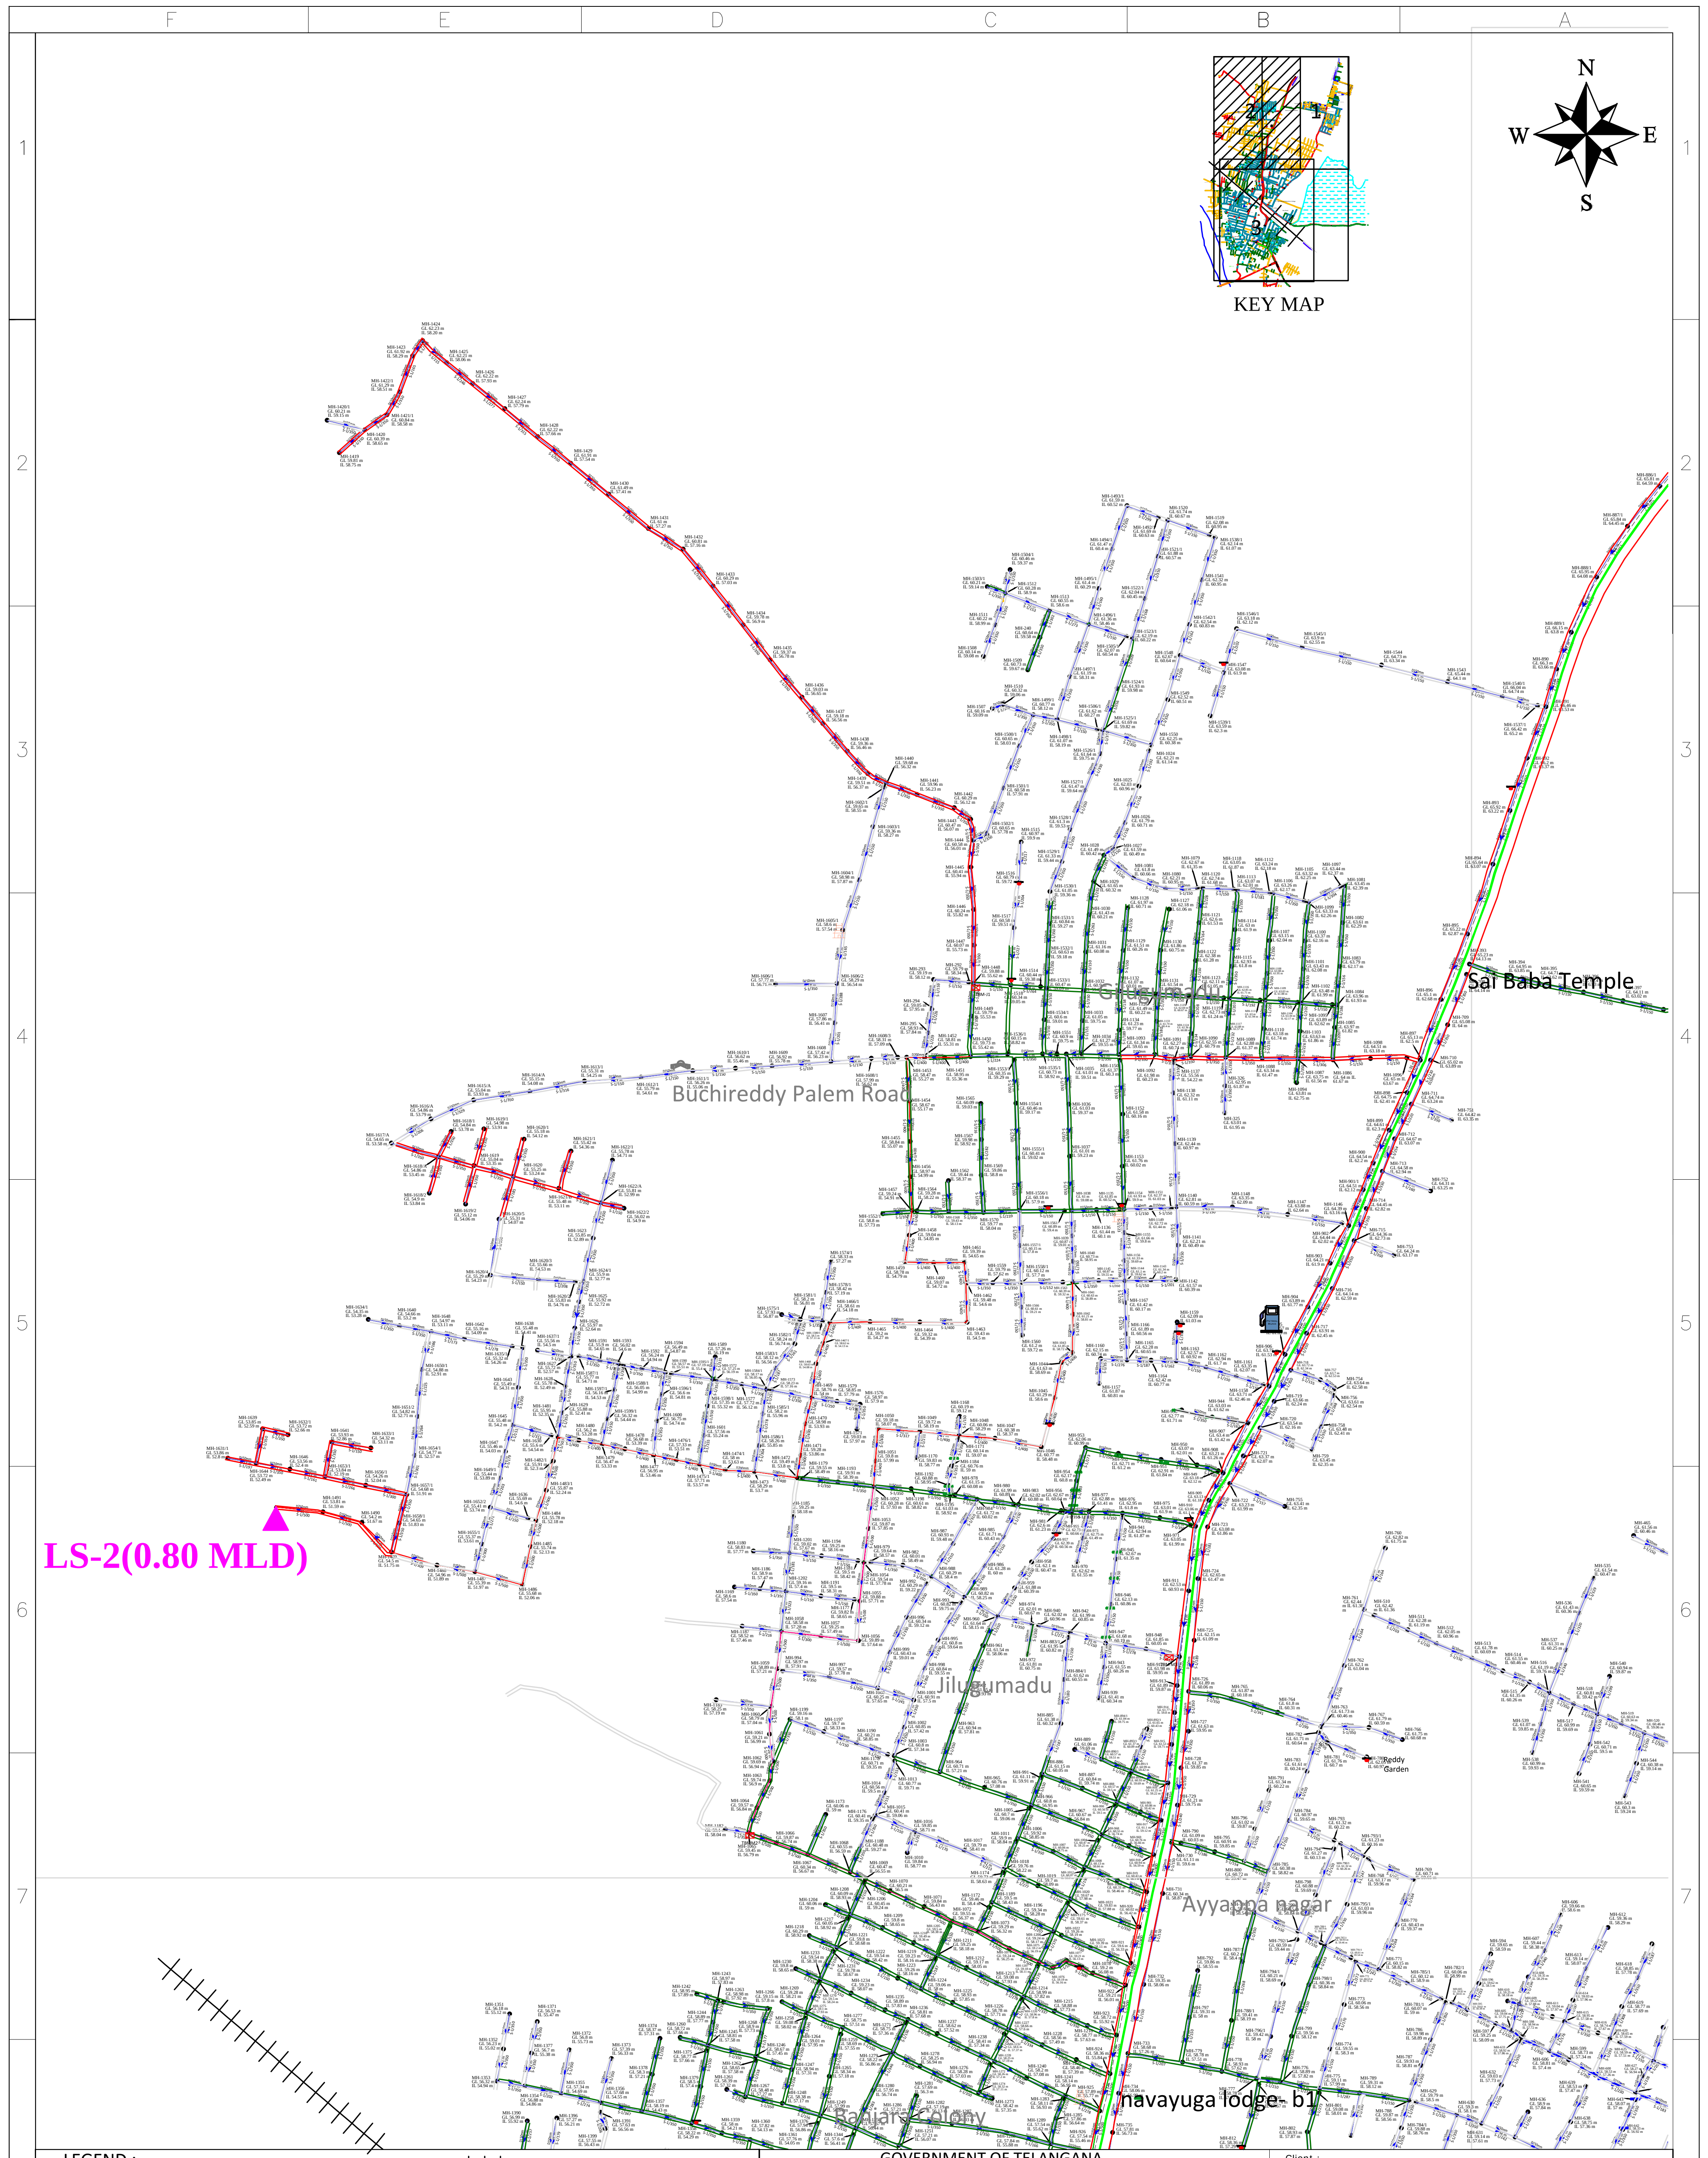

LEGEND :

BORE	BORE SOURCE	CHURCH		RAILWAY LINE	┼┼┼	🟥	300mmRCCNP3
WATER TAP		MASJID		NEW PRO. ALIGMENT	🟥	🟩	350mmRCCNP3
HAND PUMP		TEMPLE		BT ROAD	▬	🟩	400mmRCCNP3
TRAFORMER	TRANSFORMER	SCHOOL		CC ROAD	▬	🟦	150mmDWC
HT LINE TOWER		FILLING STATIO		GRAVEL ROAD	🟧	🟥	200mmDWC
ELECTRICAL POLE		CELL TOWER		MT ROAD	🟦	🟥	250mmDWC
PS	●	Lifting St(LS) ▲		STP	🟦	🟩	600mmRCCNP3
						🟧	700mmRCCNP3

GOVERNMENT OF TELANGANA
PUBLIC HEALTH MUNICIPAL ENGINEERING DEPARTMENT
Superintending Engineer (PH), Warangal

PROJECT NAME : PROVIDING UNDER GROUND DRAINAGE SCHEME
IN MADHIRA MUNICIPALITY KHAMMAM DISTRICT

MILESTONE : FOR APPROVAL

Client : GOVERNMENT OF TELANGANA
PUBLIC HEALTH MUNICIPAL ENGINEERING DEPARTMENT
MADHIRA MUNICIPALITY, KHAMMAM DISTRICT

Project : PROVIDING UNDER GROUND DRAINAGE SCHEME
IN MADHIRA MUNICIPALITY KHAMMAM DISTRICT

Title : SEWERNETWORK OF ZONE-1 FOR 5.0 MLD STP

Agency: KRUSHI INFRAS INDIA PVT.LTD.
HYDERABAD
Ph: 9395550784
Email: Krushiinfrasindia@gmail.com

SHEET -2/3

F E D C B A

8

🟥	300mmRCCNP3
🟩	350mmRCCNP3
🟩	400mmRCCNP3
🟦	150mmDWC
🟥	200mmDWC
🟩	600mmRCCNP3
🟧	700mmRCCNP3

Lifting St(LS) ▲