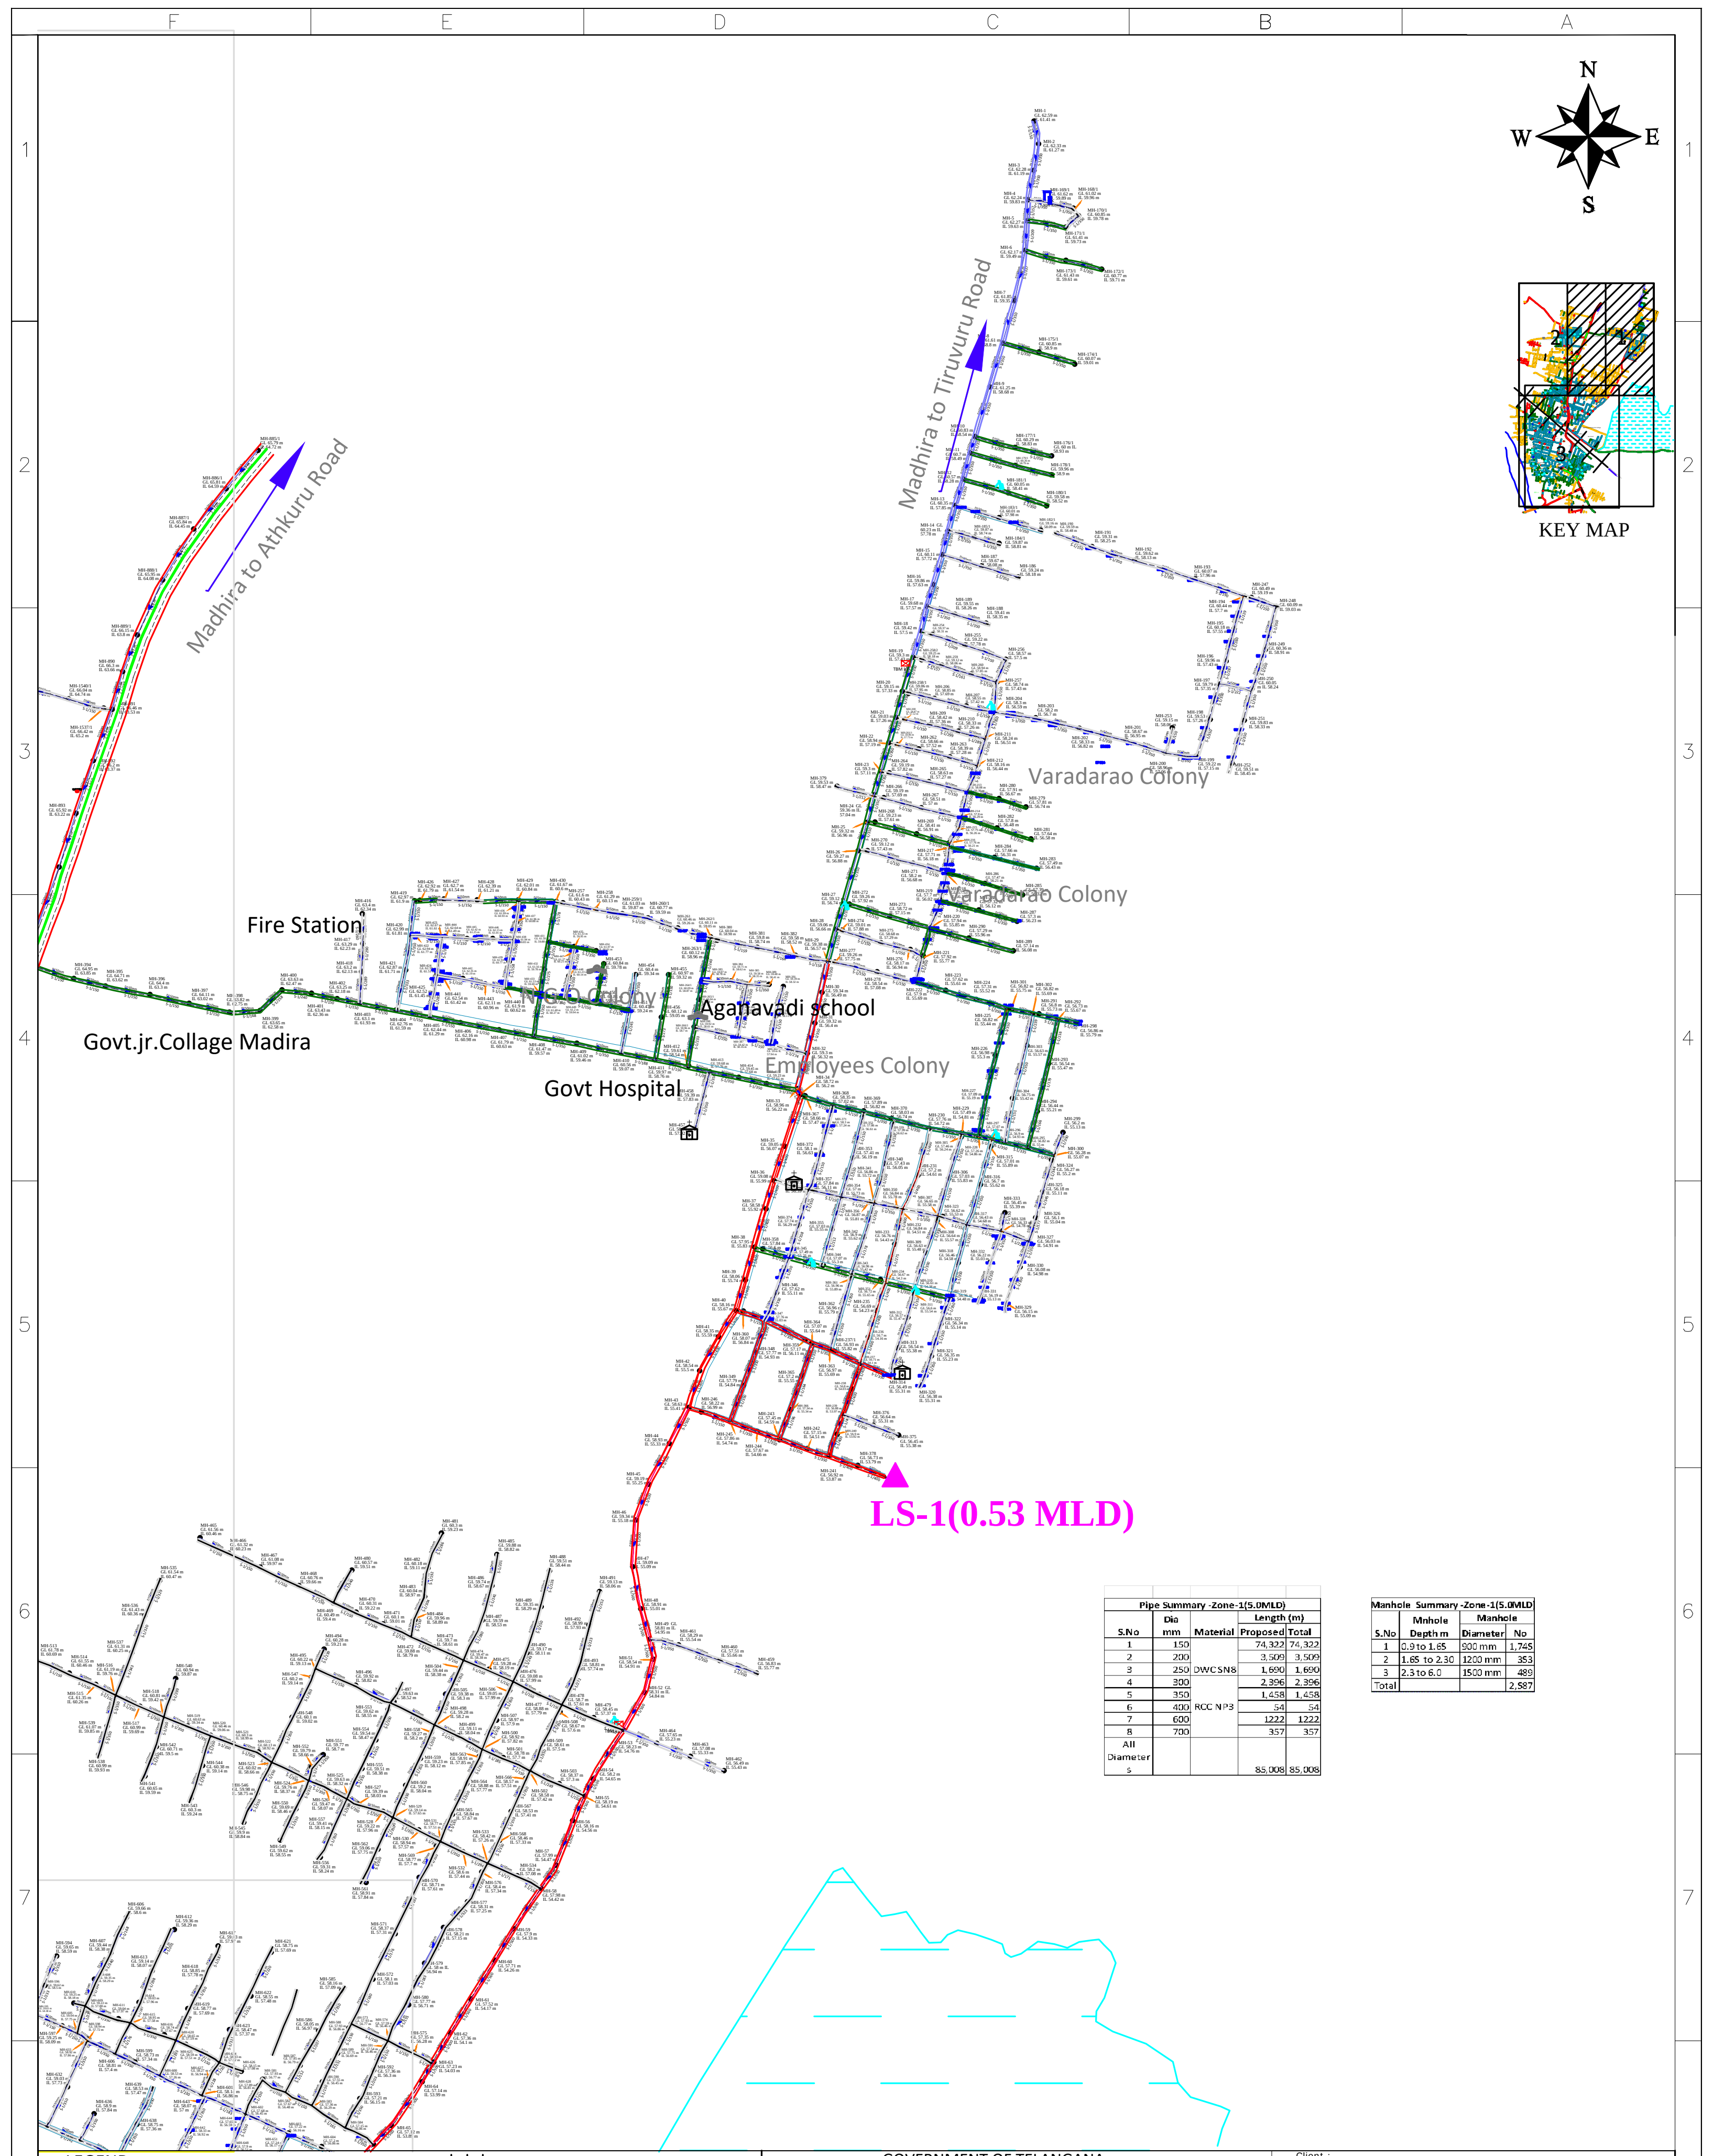

Pipe Summary -Zone-1(5.0MLD)				
S.No	Dia mm	Material	Length (m)	
			Proposed	Total
1	150		74,322	74,322
2	200		3,509	3,509
3	250	DWCSN8	1,690	1,690
4	300		2,396	2,396
5	350		1,458	1,458
6	400	RCC NP3	54	54
7	600		1222	1222
8	700		357	357
All Diameters			85,008	85,008

Manhole Summary -Zone-1(5.0MLD)			
S.No	Mnhole Depth m	Manhole	
		Diameter	No
1	0.9 to 1.65	900 mm	1,745
2	1.65 to 2.30	1200 mm	353
3	2.3 to 6.0	1500 mm	489
Total			2,587

LEGEND :

BORE		CHURCH		RAILWAY LINE	300mmRCCNP3
WATER TAP		MASJID		NEW PRO. ALIGMENT	350mmRCCNP3
HAND PUMP		TEMPLE		BT ROAD	400mmRCCNP3
TRAFORMER		SCHOOL		CC ROAD	150mmDWC
HT LINE TOWER		FILLING STATIO		GRAVEL ROAD	200mmDWC
ELECTRICAL POLE		CELL TOWER		MT ROAD	250mmDWC
PS	●	Lifting St(LS)	▲	STP	600mmRCCNP3
					700mmRCCNP3

GOVERNMENT OF TELANGANA
PUBLIC HEALTH MUNICIPAL ENGINEERING DEPARTMENT
Superintending Engineer (PH), Warangal

PROJECT NAME : PROVIDING UNDER GROUND DRAINAGE SCHEME IN MADHIRA MUNICIPALITY KHAMMAM DISTRICT

MILESTONE : FOR APPROVAL

Client : GOVERNMENT OF TELANGANA
PUBLIC HEALTH MUNICIPAL ENGINEERING DEPARTMENT
MADHIRA MUNICIPALITY, KHAMMAM DISTRICT

Project : PROVIDING UNDER GROUND DRAINAGE SCHEME IN MADHIRA MUNICIPALITY KHAMMAM DISTRICT

Title : SEWERNETWORK OF ZONE-1 FOR 5.0 MLD STP

Agency: KRUSHI INFRAS INDIA PVT.LTD.
HYDERABAD
Ph: 9395550784
Email: Krushiinfrasindia@gmail.com

SHEET -1/3

300mmRCCNP3
350mmRCCNP3
400mmRCCNP3
150mmDWC
200mmDWC
600mmRCCNP3
700mmRCCNP3

Lifting St(LS)▲