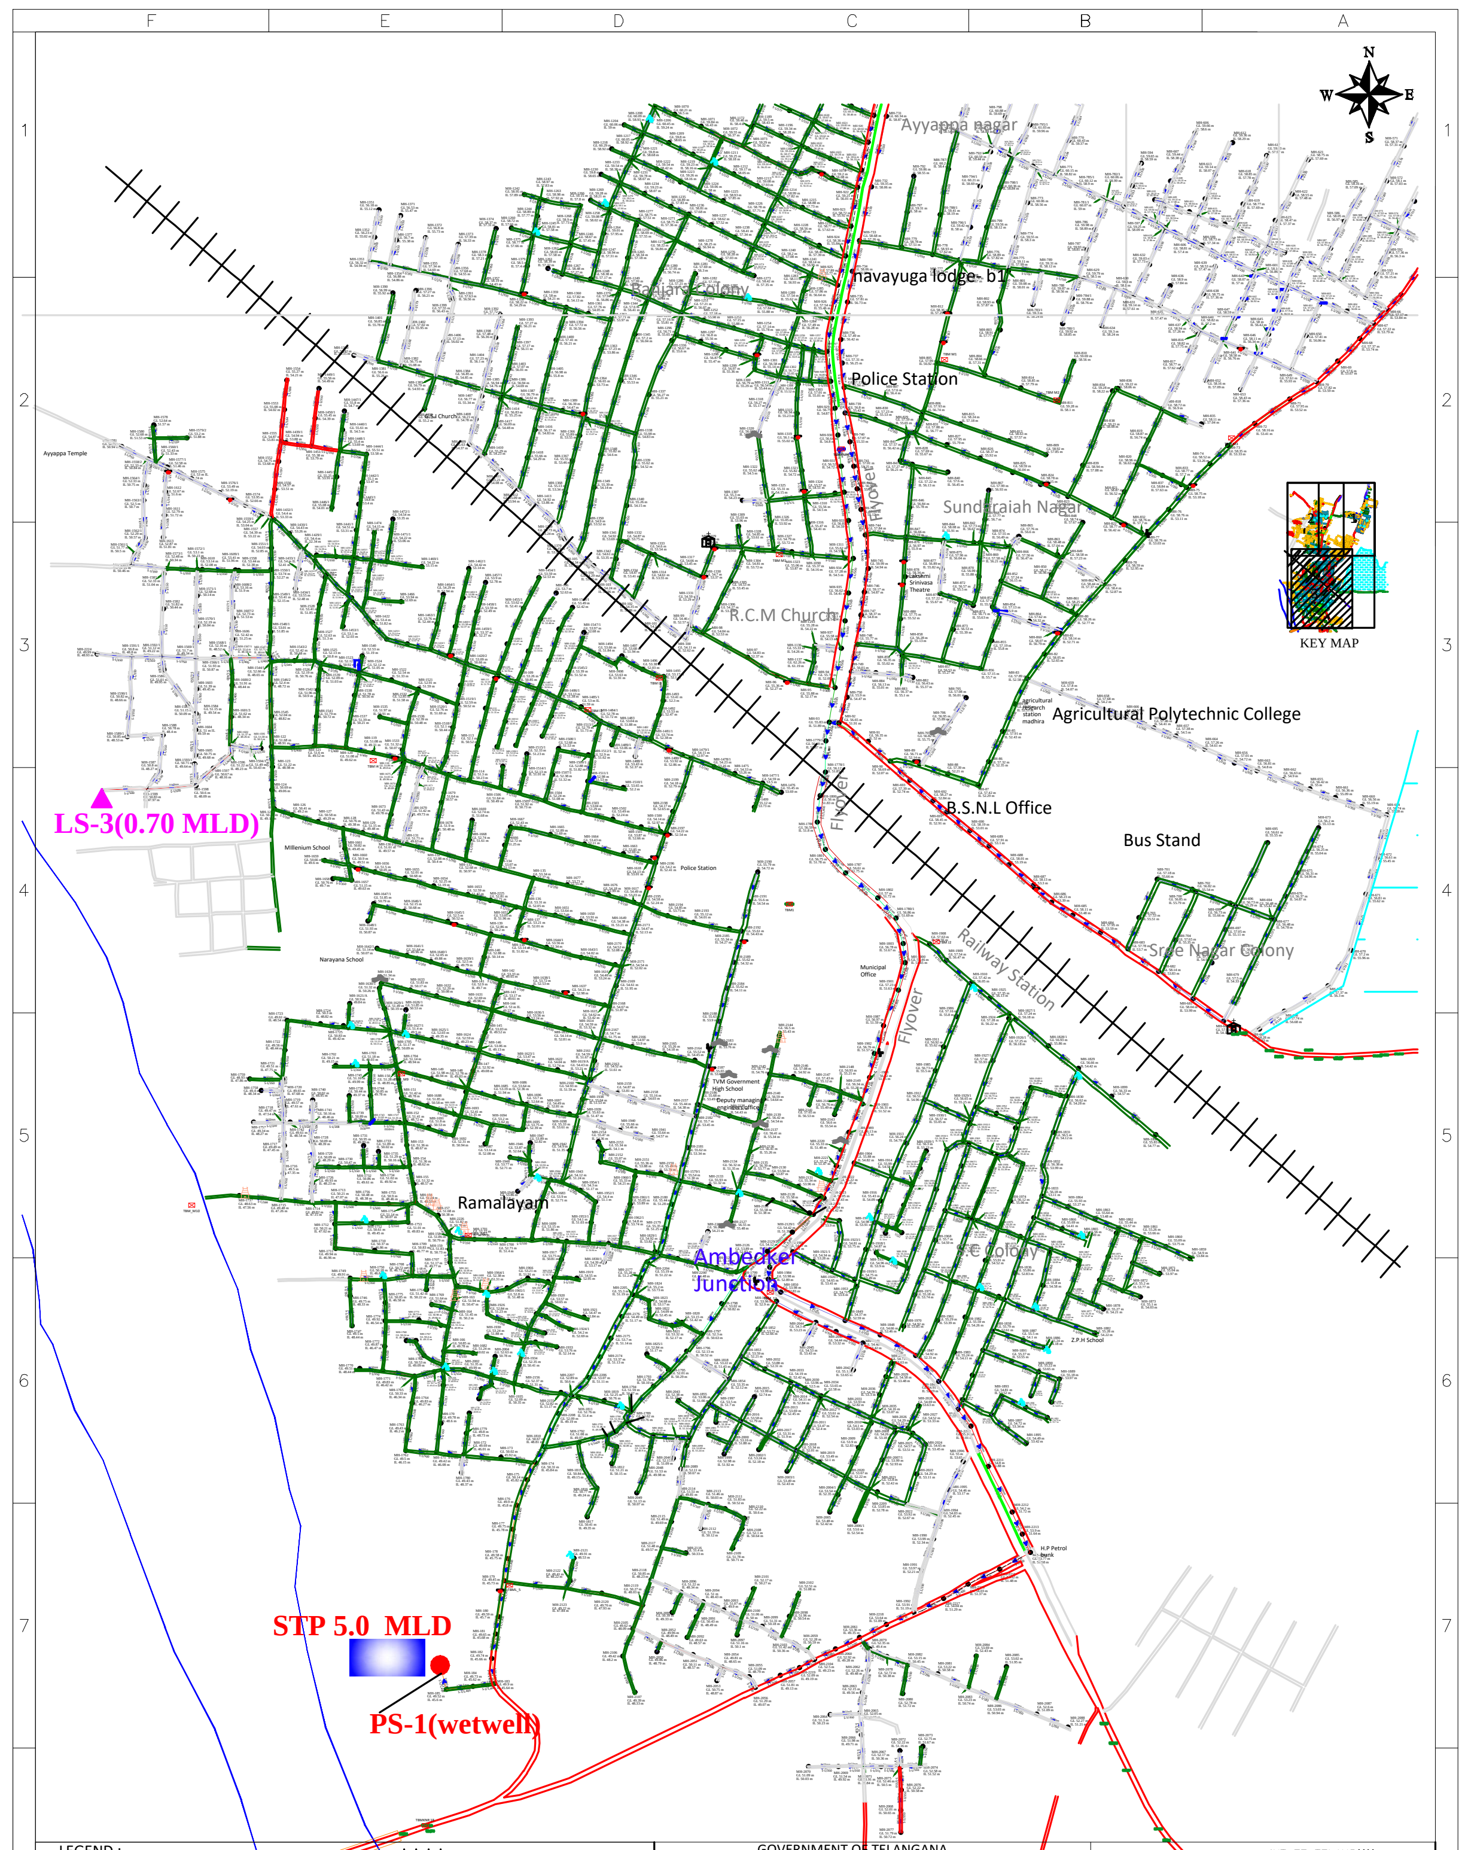

LEGEND :

BORE		CHURCH		RAILWAY LINE			300mmRCCNP3
WATER TAP		MASJID		NEW PRO. ALIGMENT			350mmRCCNP3
HAND PUMP		TEMPLE		BT ROAD			400mmRCCNP3
TRAFORMER		SCHOOL		CC ROAD			150mmDWC 200mmDWC
HT LINE TOWER		FILLING STATIO		GRAVEL ROAD			250mmDWC
ELECTRICAL POLE		CELL TOWER		MT ROAD			600mmRCCNP3
PS	●	Lifting St(LS)	▲	STP			700mmRCCNP3

GOVERNMENT OF TELANGANA
PUBLIC HEALTH MUNICIPAL ENGINEERING DEPARTMENT
Superintending Engineer (PH), Warangal

PROJECT NAME : PROVIDING UNDER GROUND DRAINAGE SCHEME IN MADHIRA MUNICIPALITY KHAMMAM DISTRICT

MILESTONE : FOR APPROVAL

Client : GOVERNMENT OF TELANGANA
PUBLIC HEALTH MUNICIPAL ENGINEERING DEPARTMENT
MADHIRA MUNICIPALITY, KHAMMAM DISTRICT

Project : PROVIDING UNDER GROUND DRAINAGE SCHEME
IN MADHIRA MUNICIPALITY KHAMMAM DISTRICT

Title : SEWERNETWORK OF ZONE-1 FOR 5.0 MLD STP

Agency: KRUSHI INFRAS INDIA PVT.LTD.
HYDERABAD

Ph: 9395550784
Email: Krushiinfrasindia@gmail.com

SHEET -3/3