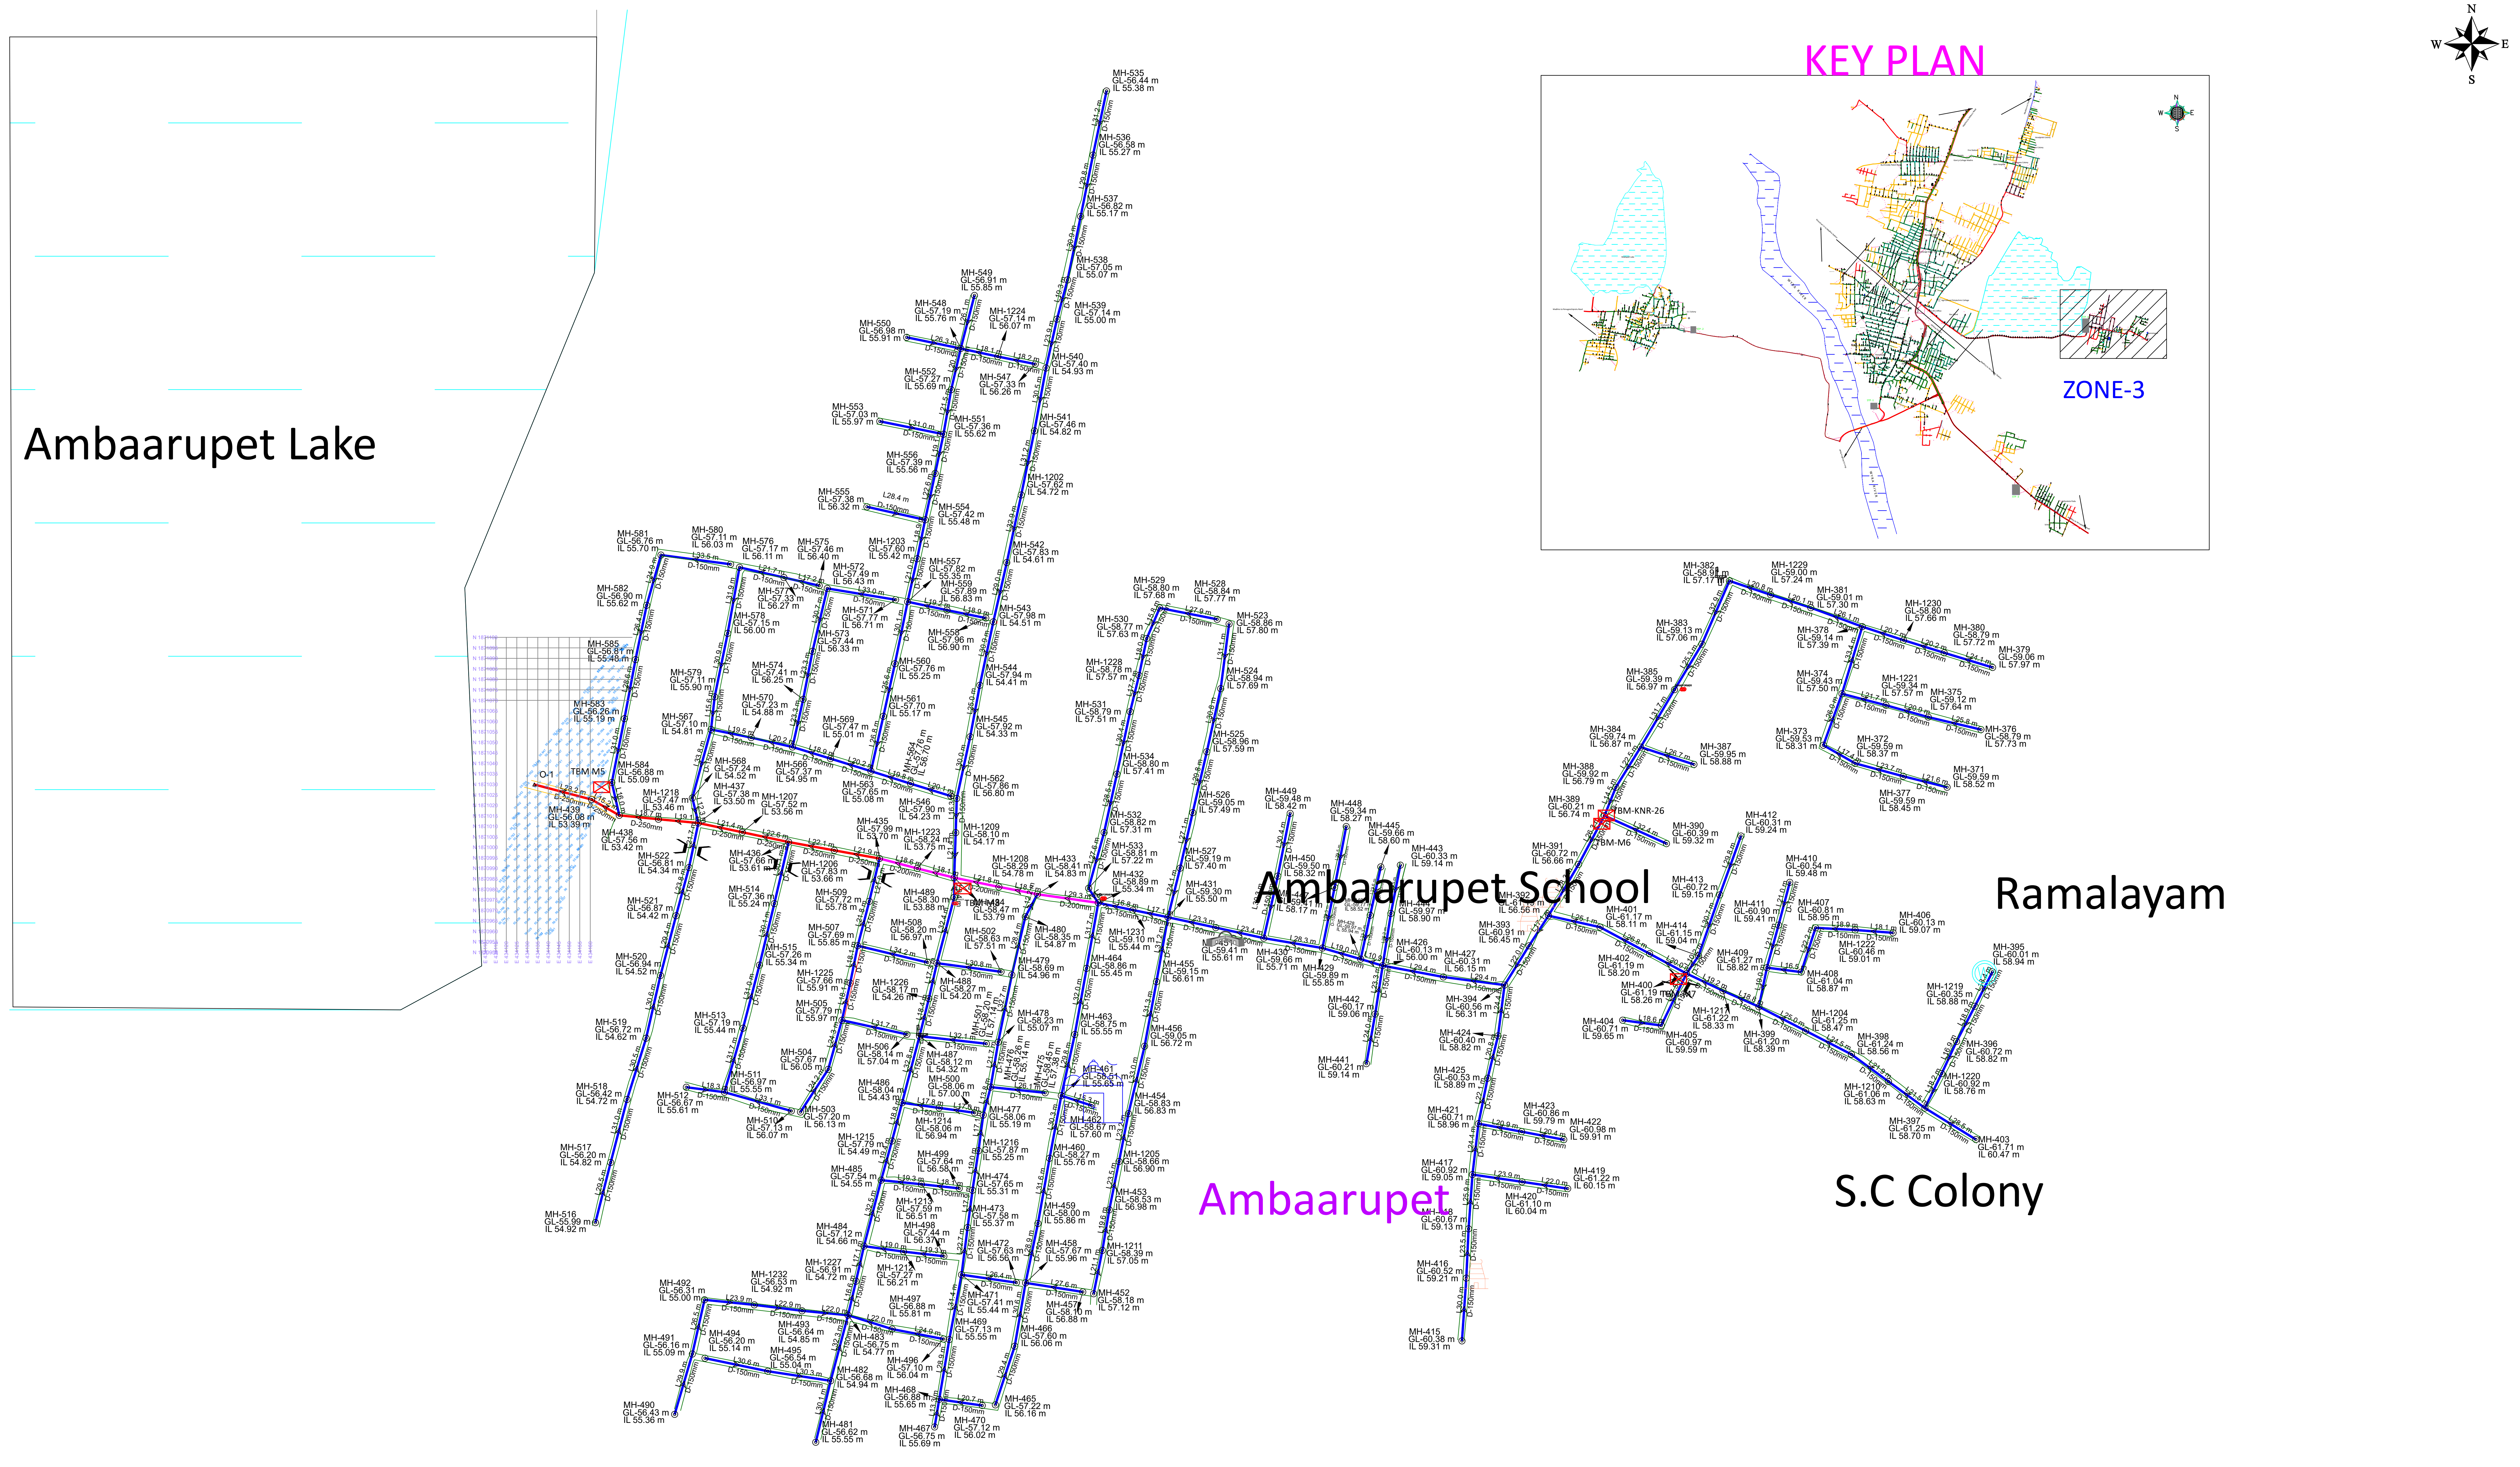

LEGEND :

- BORE
- WATER TAP
- HAND PUMP
- TRAFORMER
- HT LINE TOWER
- ELECTRICAL POLE
- FILLING STATIO
- CELL TOWER
- PS ●
- Lifting St(LS) ▲
- BT ROAD
- CC ROAD
- GRAVEL ROAD
- MT ROAD
- STP
- pipe 150 mm
- pipe 200 mm
- pipe 250 mm

PUBLIC HEALTH MUNICIPAL ENGINEERING DEPARTMENT
Superintending Engineer (PH), Warangal

PROJECT NAME : PROVIDING UNDER GROUND DRAINAGE SCHEME
IN MADHIRA MUNICIPALITY KHAMMAM DISTRICT

MILESTONE : FOR APPROVAL

Client :
GOVERNMENT OF TELANGANA
PUBLIC HEALTH MUNICIPAL ENGINEERING DEPARTMENT
MADHIRA MUNICIPALITY, KHAMMAM DISTRICT

Project : PROVIDING UNDER GROUND DRAINAGE SCHEME
IN MADHIRA MUNICIPALITY KHAMMAM DISTRICT

Title : **SEWERNETWORK OF ZONE-3 FOR 0.4 MLD STP**

Consultant: BRANDEN CONSULTANCY PVT.LTD. VISAKHAPATNAM.

Agency: KRUSHI INFRAS INDIA PVT.LTD.
Ph: 9395550784
Email: Krushiinfrasindia@gmail.com

SHEET -1