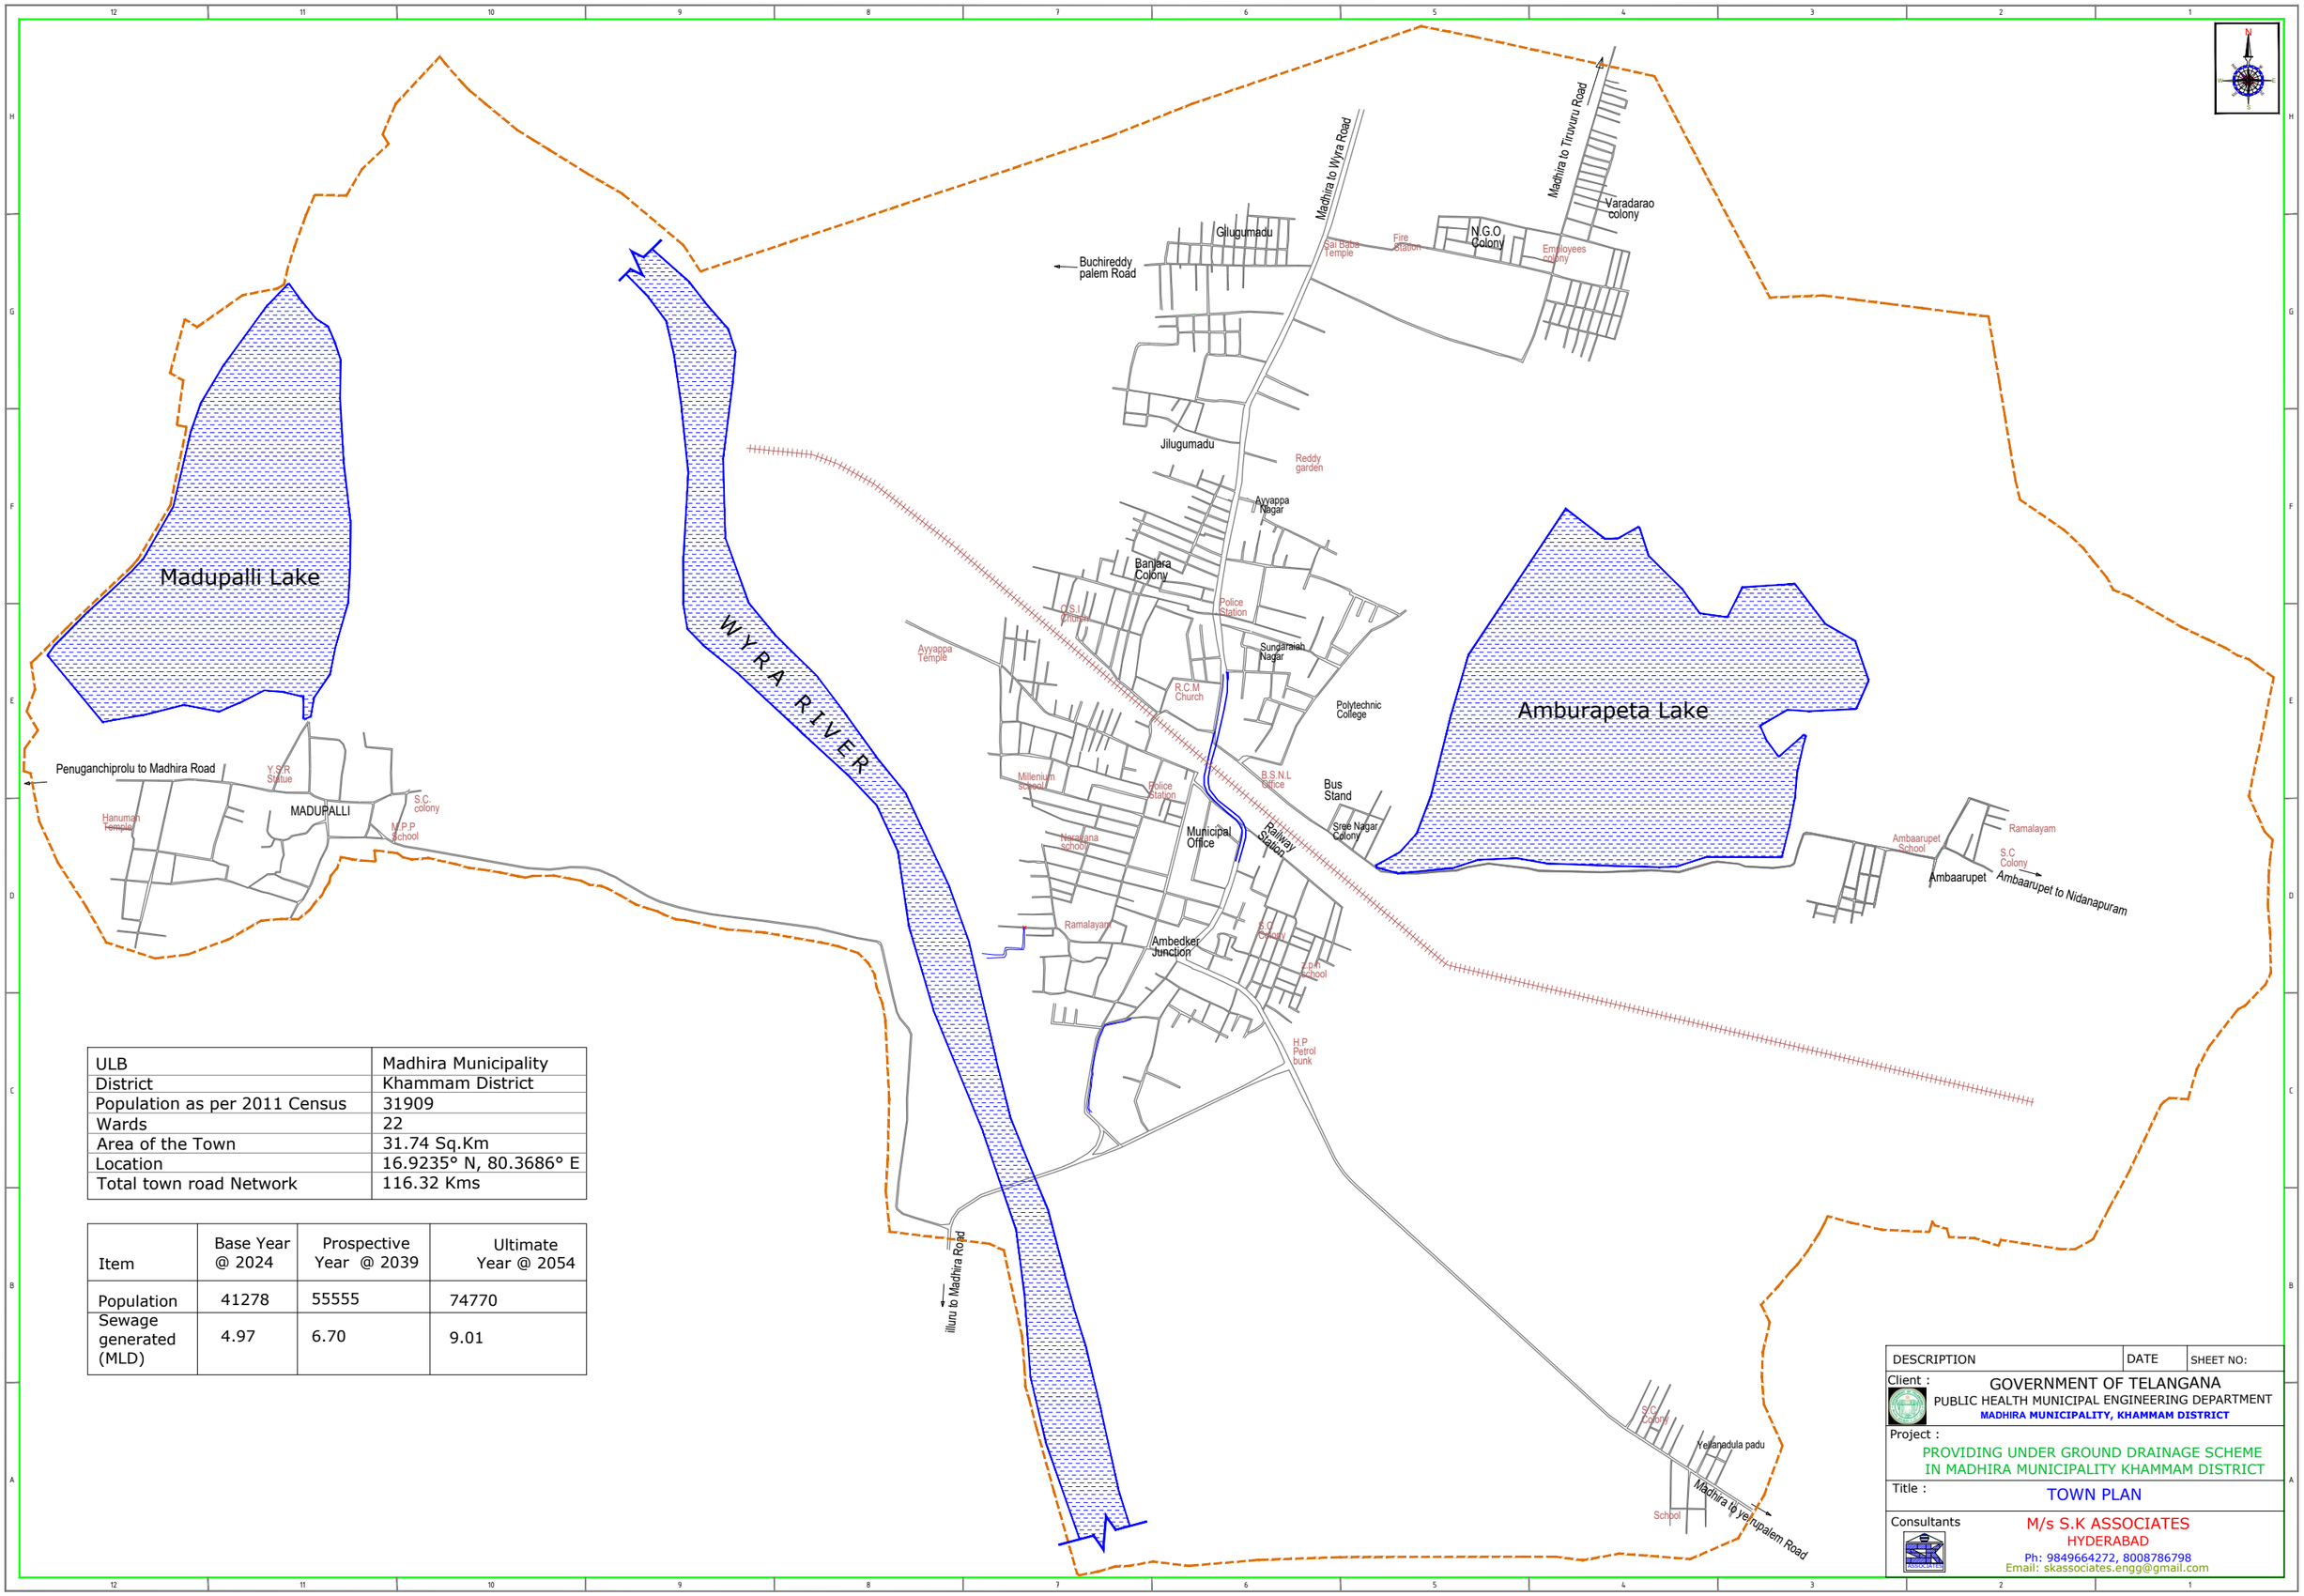


ULB	Madhira Municipality
District	Khammam District
Population as per 2011 Census	31909
Wards	22
Area of the Town	31.74 Sq.Km
Location	16.9235° N, 80.3686° E
Total town road Network	116.32 Kms

Item	Base Year @ 2024	Prospective Year @ 2039	Ultimate Year @ 2054
Population	41278	55555	74770
Sewage generated (MLD)	4.97	6.70	9.01

DESCRIPTION	DATE	SHEET NO:

Client :
GOVERNMENT OF TELANGANA
PUBLIC HEALTH MUNICIPAL ENGINEERING DEPARTMENT
MADHIRA MUNICIPALITY, KHAMMAM DISTRICT

Project :
PROVIDING UNDER GROUND DRAINAGE SCHEME IN MADHIRA MUNICIPALITY KHAMMAM DISTRICT

Title :
TOWN PLAN

Consultants
M/s S.K ASSOCIATES
HYDERABAD
Ph: 9849664272, 8008786798
Email: skassociates.engg@gmail.com