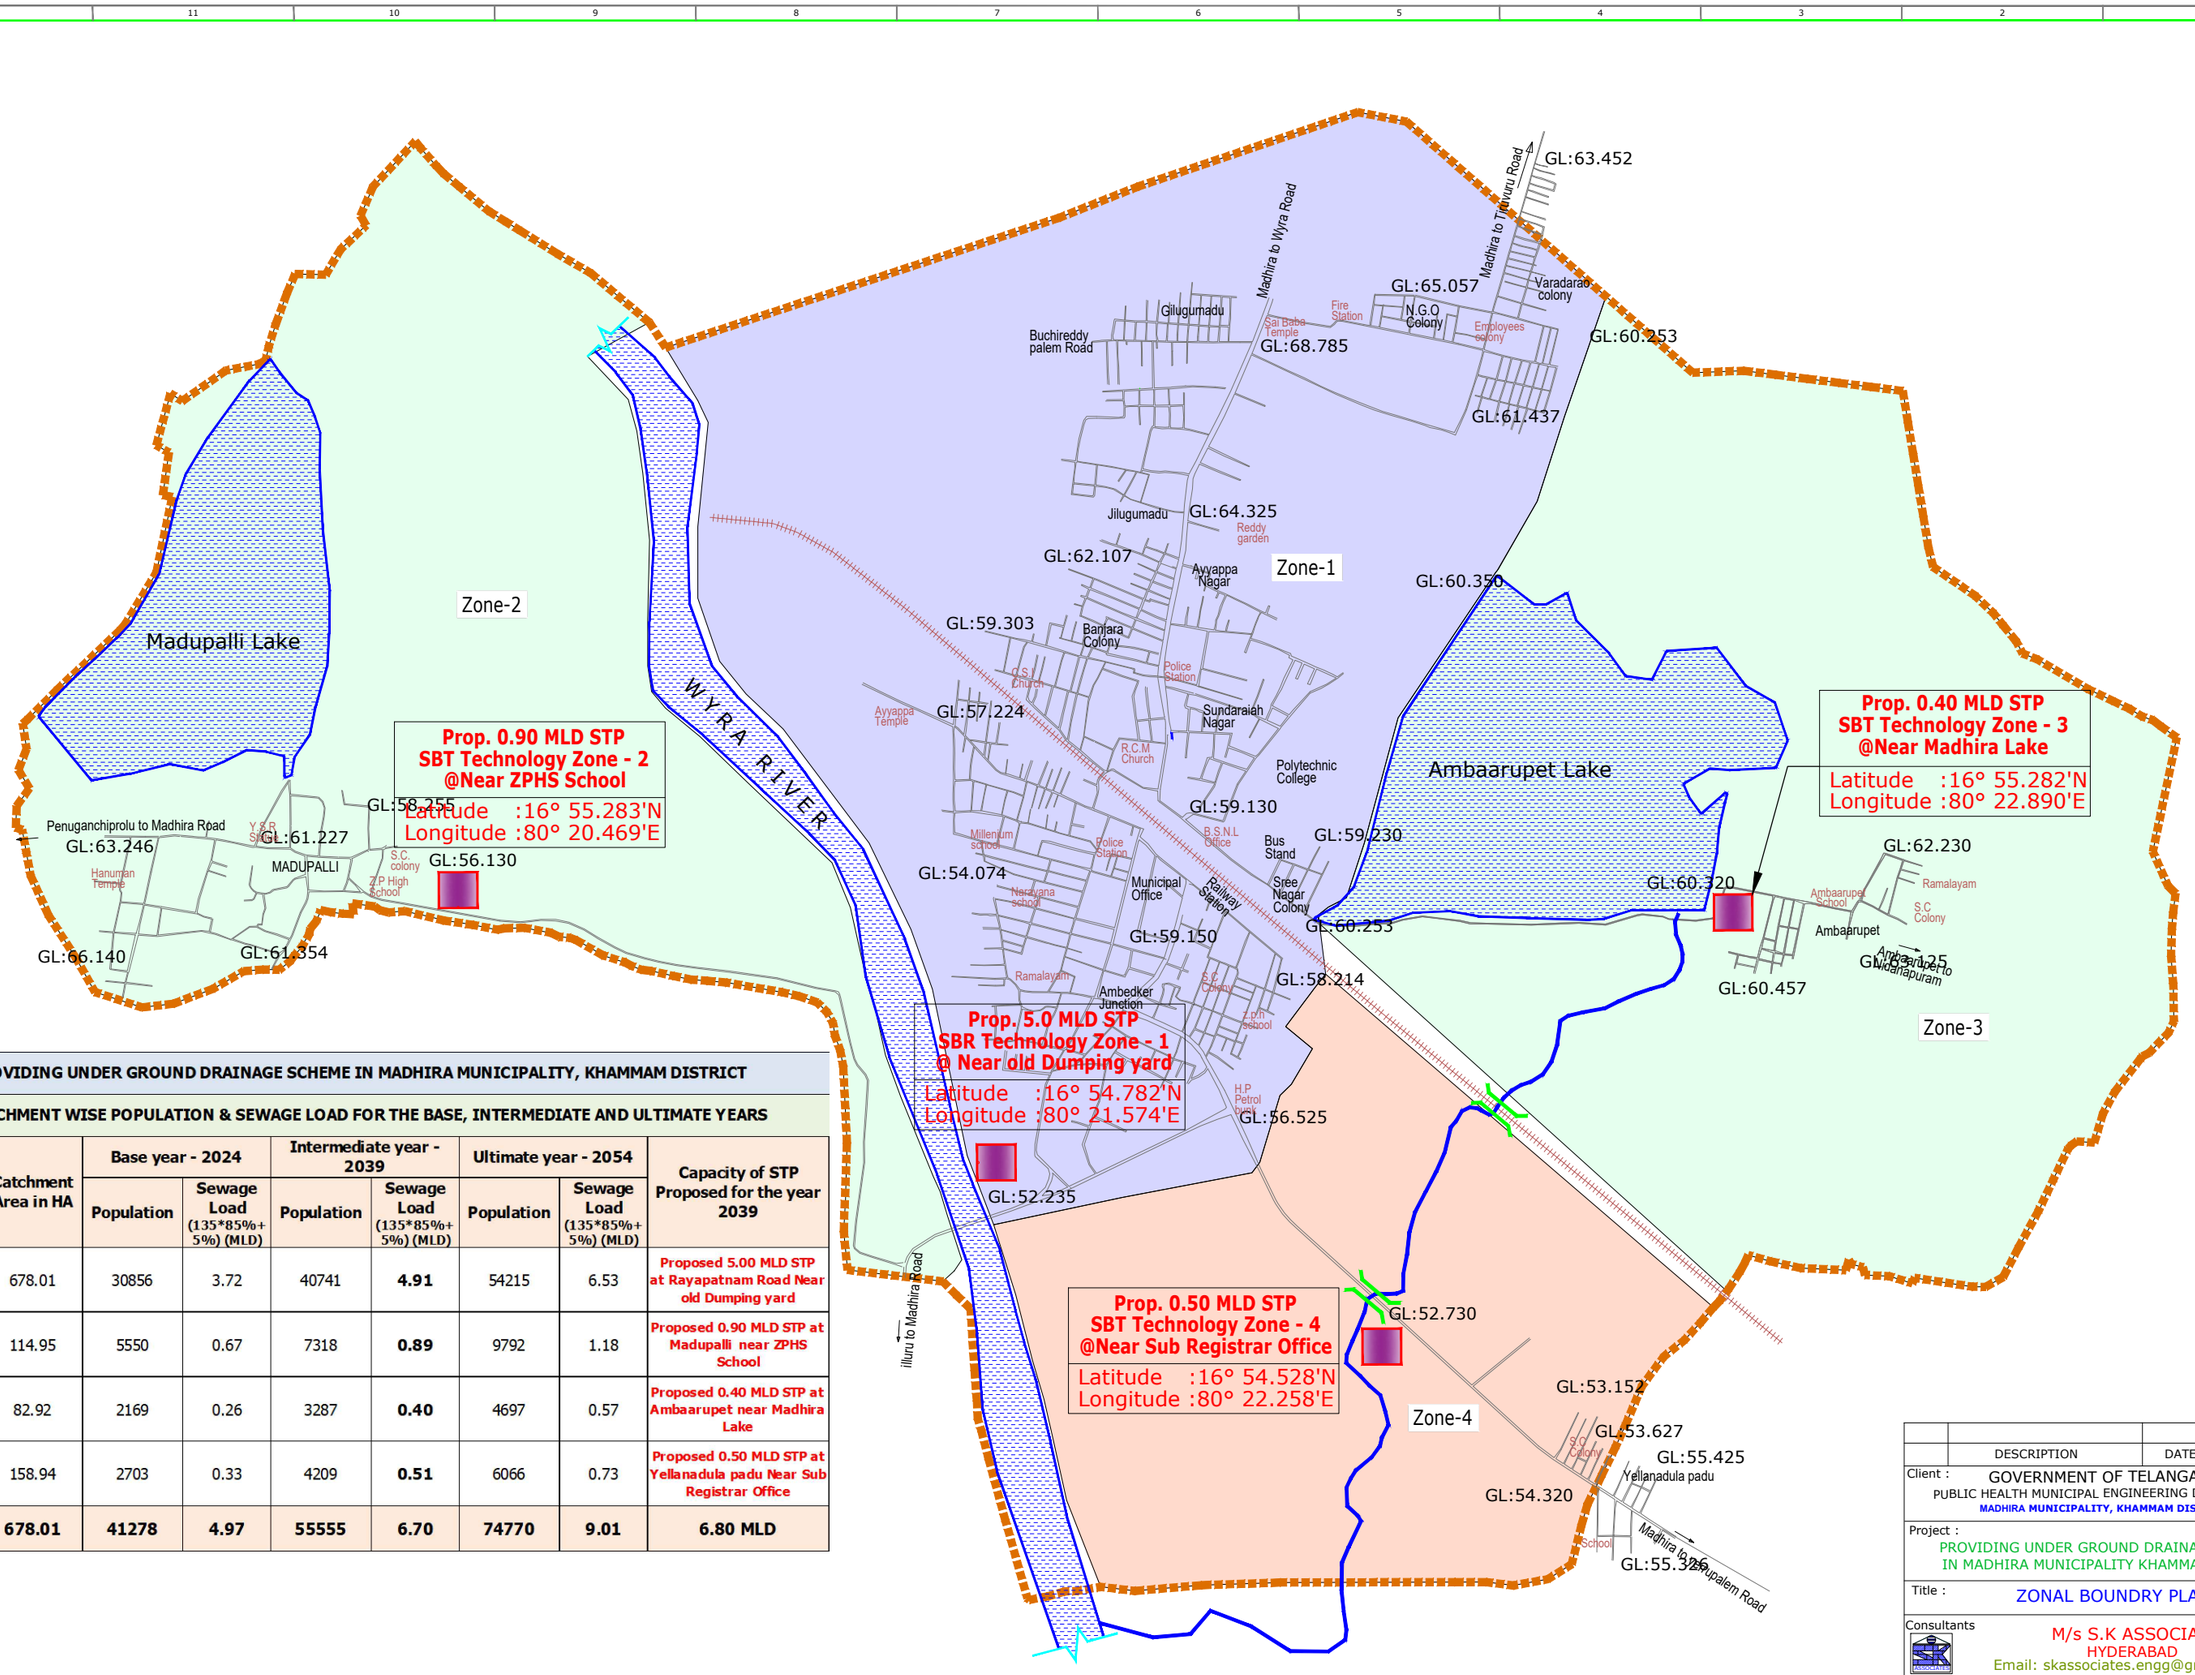


PROVIDING UNDER GROUND DRAINAGE SCHEME IN MADHIRA MUNICIPALITY, KHAMMAM DISTRICT

CATCHMENT WISE POPULATION & SEWAGE LOAD FOR THE BASE, INTERMEDIATE AND ULTIMATE YEARS

Zone	Catchment Area in HA	Base year - 2024		Intermediate year - 2039		Ultimate year - 2054		Capacity of STP Proposed for the year 2039
		Population	Sewage Load (135*85%+5%) (MLD)	Population	Sewage Load (135*85%+5%) (MLD)	Population	Sewage Load (135*85%+5%) (MLD)	
Zone - 1	678.01	30856	3.72	40741	**4.91**	54215	6.53	Proposed 5.00 MLD STP at Rayapatnam Road Near old Dumping yard
Zone-2	114.95	5550	0.67	7318	**0.89**	9792	1.18	Proposed 0.90 MLD STP at Madupalli near ZPHS School
Zone-3	82.92	2169	0.26	3287	**0.40**	4697	0.57	Proposed 0.40 MLD STP at Ambaarupet near Madhira Lake
Zone-4	158.94	2703	0.33	4209	**0.51**	6066	0.73	Proposed 0.50 MLD STP at Yellanadula padu Near Sub Registrar Office
Total	**678.01**	**41278**	**4.97**	**55555**	**6.70**	**74770**	**9.01**	**6.80 MLD**

			SHEET NO:
	DESCRIPTION	DATE	REMARKS

Client : GOVERNMENT OF TELANGANA
PUBLIC HEALTH MUNICIPAL ENGINEERING DEPARTMENT
MADHIRA MUNICIPALITY, KHAMMAM DISTRICT

Project : PROVIDING UNDER GROUND DRAINAGE SCHEME IN MADHIRA MUNICIPALITY KHAMMAM DISTRICT

Title : ZONAL BOUNDRY PLAN

Consultants
M/s S.K ASSOCIATES
HYDERABAD
Email: skassociates.engg@gmail.com